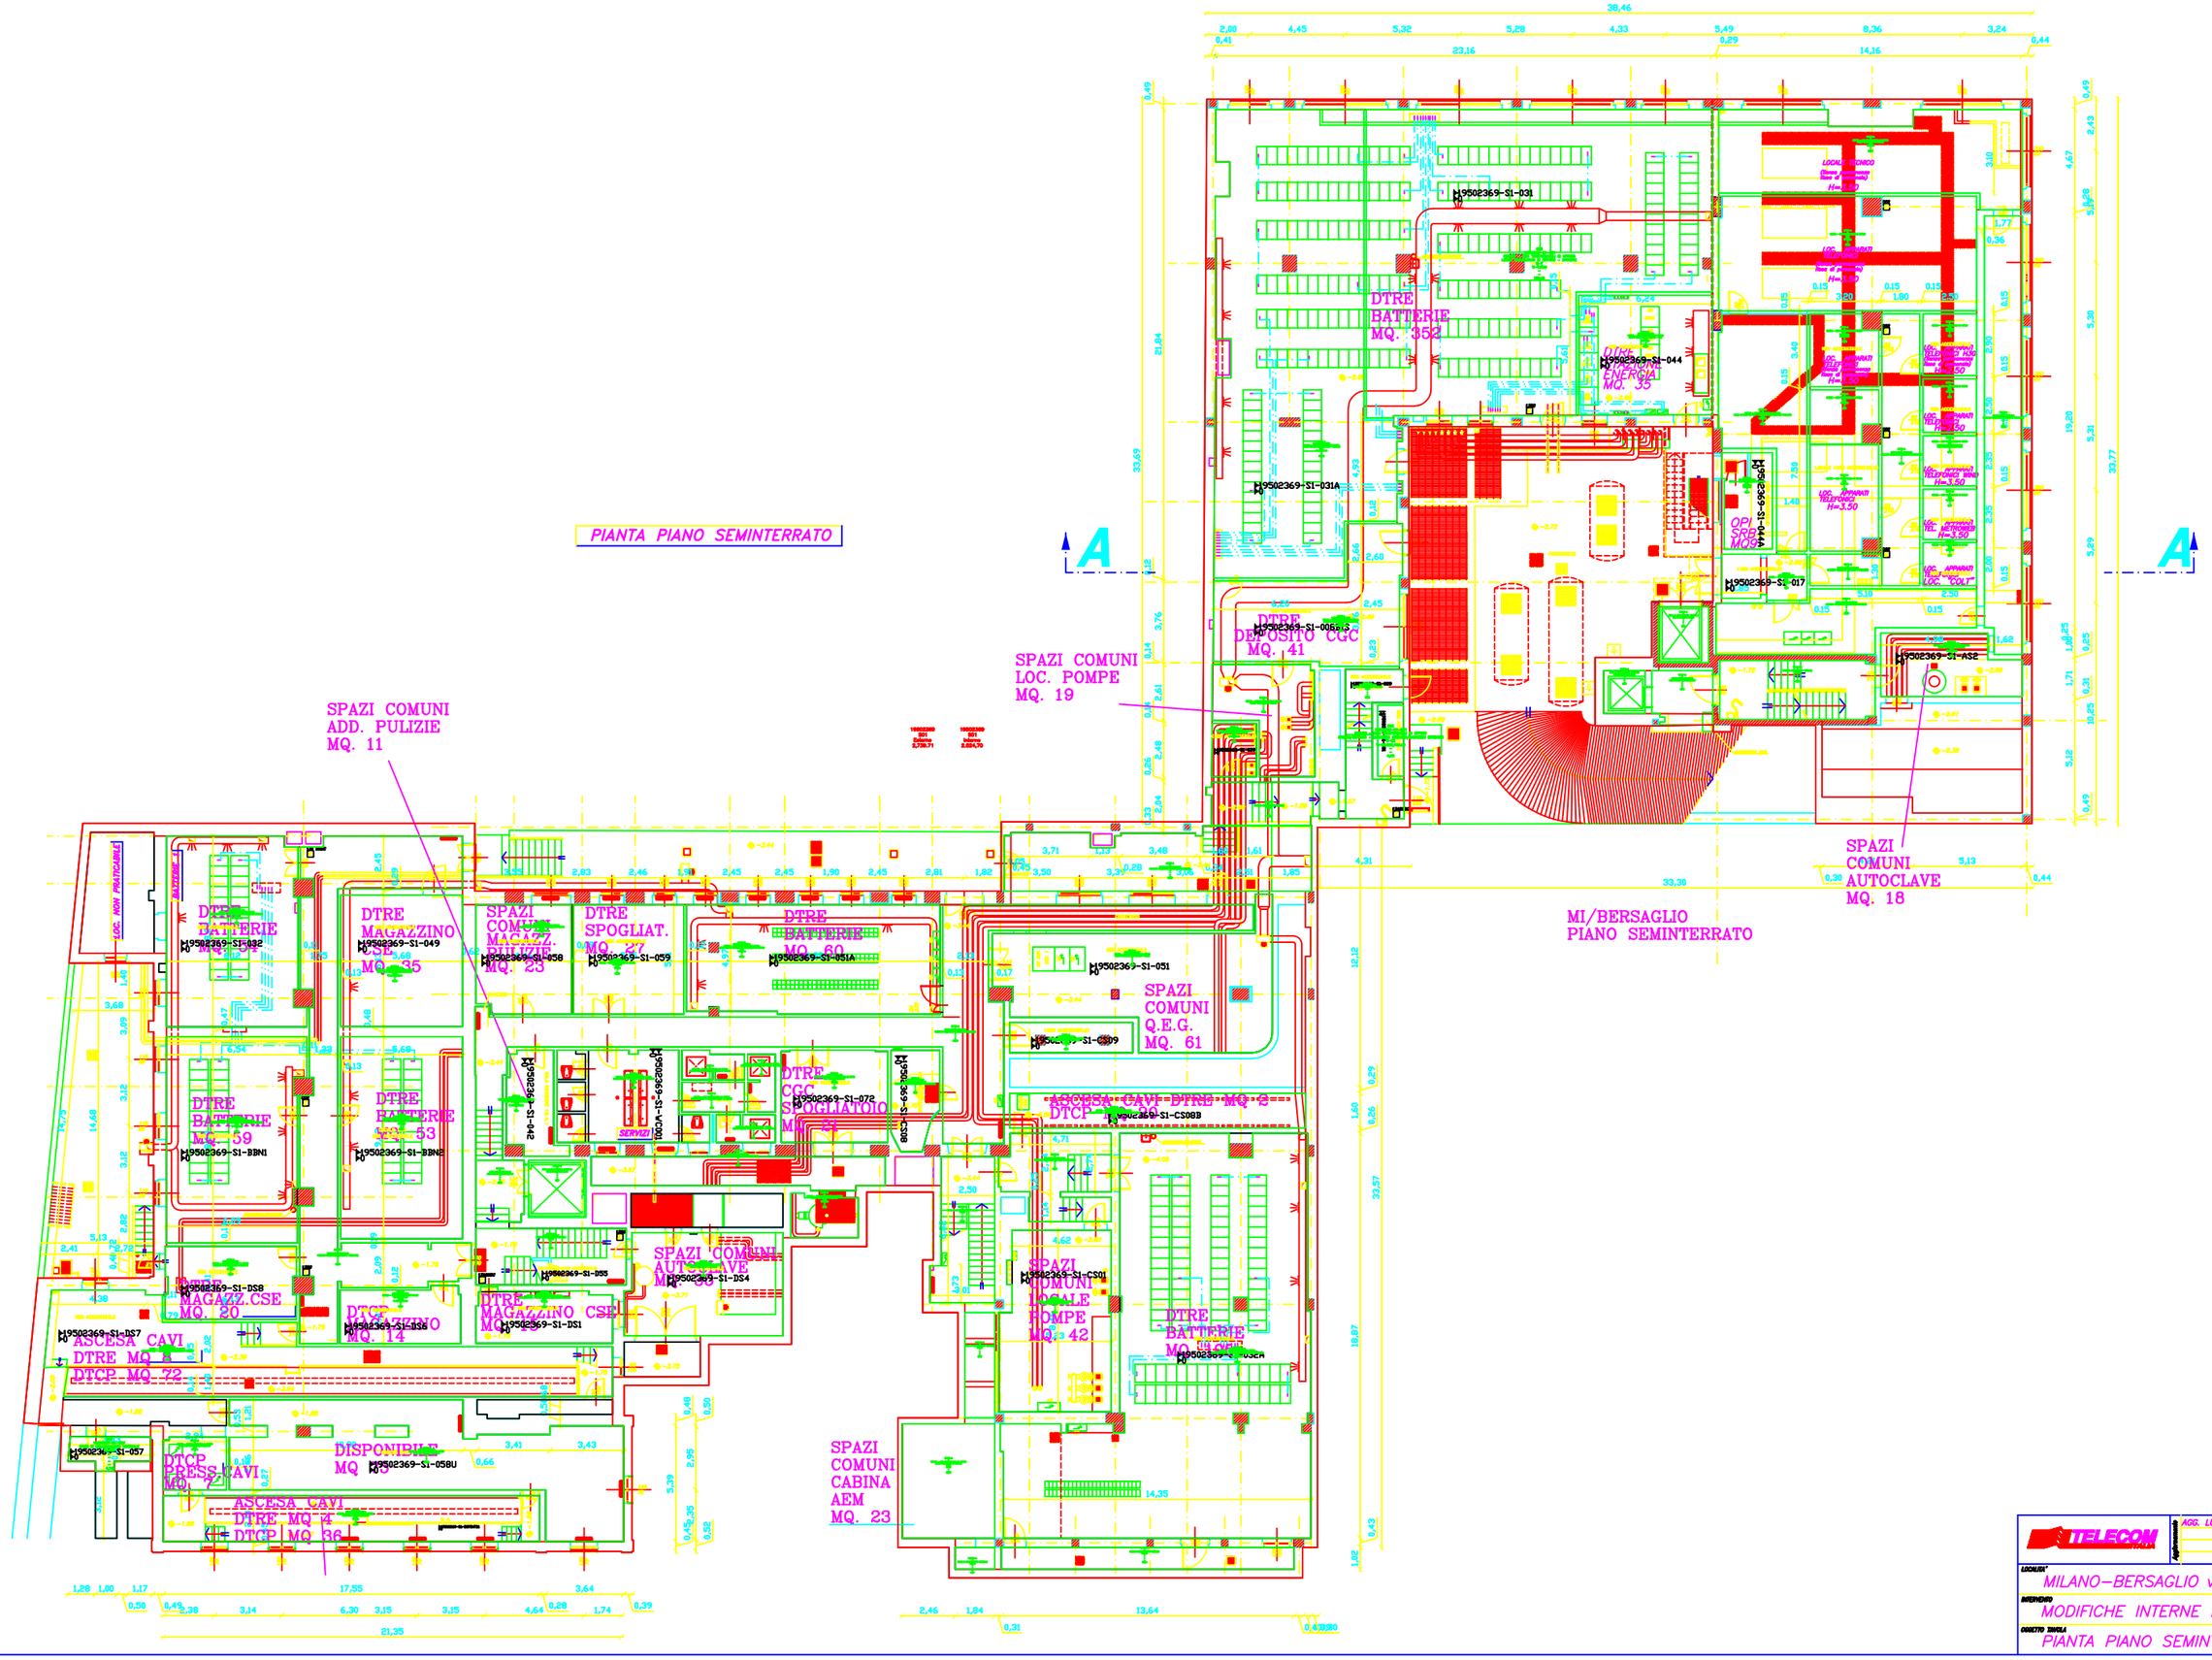

TELECOM ITALIA	AGG. LUGLIO 2001	Tavola n. BER/3
LOCALITA' MILANO–BERSAGLIO via Plana		DISEGNATO
INTERVENTO MODIFICHE INTERNE ED ESTERNE		VISTO
OGGETTO TAVOLA PIANTA PIANO SEMINTERRATO		FILE
		DATA LUGLIO '01
		FORMATO A0
		SCALA 1:100
		ESISTENTE
		DEMOLIRE
		COSTRUIRE